

DD24132-08-WP-PID-001-1

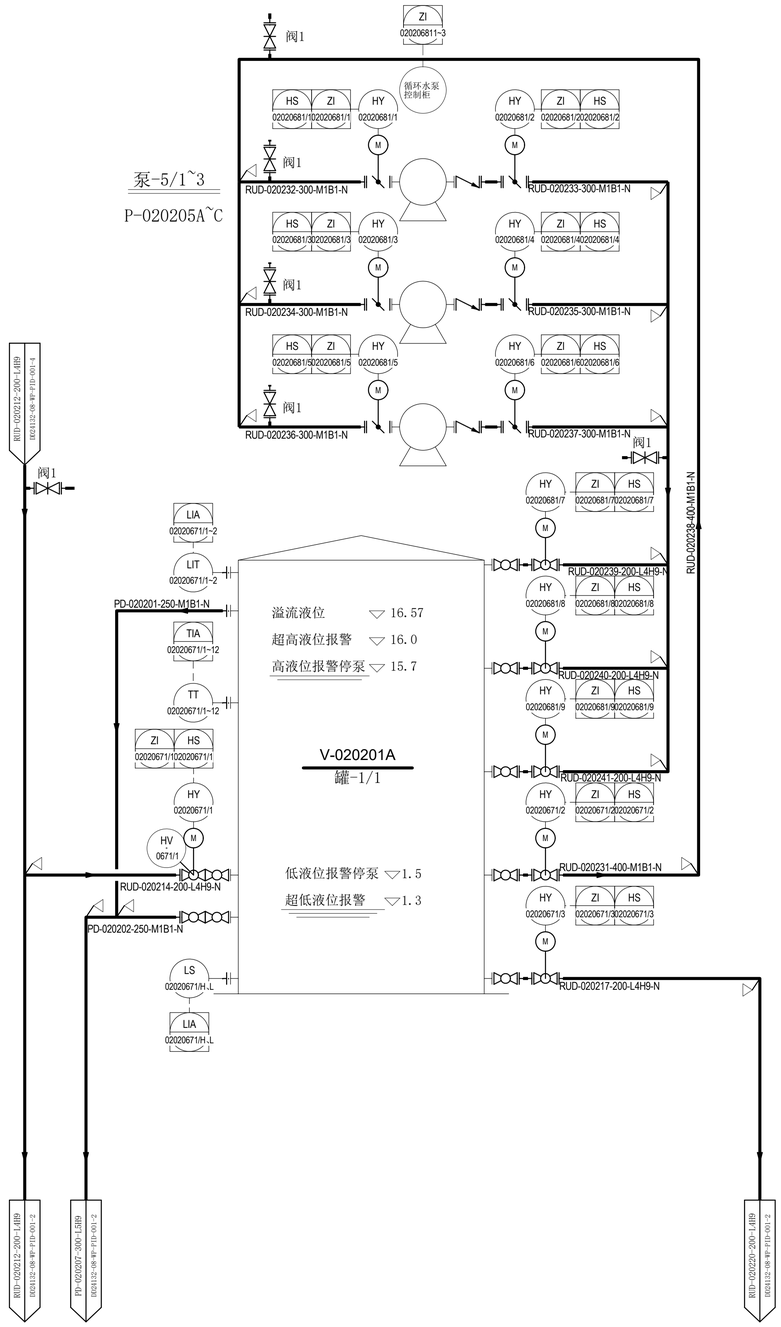

说明：

1、本流程为米北-1集气站采出水存储及装卸车区流程图。

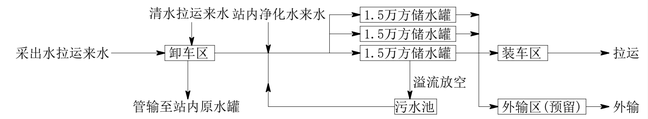

2、管线字母代号对应介质


管线、阀门编号及设备位号按照油田产建数字化交付编码规定执行。对应介质代号如下：

序号	代号	中文名称	序号	代号	中文名称
1	C	化学药剂	8	OS	含油污泥
2	RWR	循环水(回)	9	WO	污油
3	RWS	循环水(供)	10	PD	重力流排污
4	DGW	气田采出水	11	CR	地上污水罐上清液
5	TOD	处理后回注采出水	12	FRD	初期雨水
6	RW	清水	13	CRD	清洁雨水
7	RUD	回用水	14	SD	生活污水

3、字母代号功能

字母	首位功能	后继功能	字母	首位功能	后继功能
T	温 度	变 送	H	人工触发	
P	压 力		C		控 制
L	液 位		I		显 示
F	流 量		R		记 录
A	分 析	报 警	U	多变量	多功能
M	水分或湿度	中、中间	V		阀 门
S	速度或频率	开关或联锁	X	未分类	未分类
Z	状 态	驱动器、执行元件	Y		继动器、转换器

4、图形符号功能

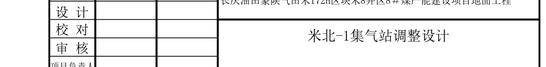

阀1	放空阀 J11H-10Q DN25	个	38	
器-1	成套加药装置(2罐2泵)	套	1	
泵-5/1~9	循环水泵 Q=400m^3/h,H=36m,N=75kW	台	9	
池-1	污水池 8mx6mx5m	座	1	
罐-1/1-3	储水罐V=15000m^3	具	3	
泵-4/1~2	污水提升泵 Q=15m^3/h,H=50m,N=5.5kW	台	2	
泵-3/1~2	装车泵 Q=120m^3/h,H=30m,N=18.5kW	台	2	
泵-2/1~2	卸水提升泵(清水) Q=120m^3/h,H=60m,N=30kW	台	2	
泵-1/1~2	卸水提升泵(采出水) Q=120m^3/h,H=60m,N=30kW	台	2	
箱-1/1-4	卸水箱 V=24m^3 6000mmx2000mmx2000mm	具	4	
编 号	名称型号及规格	单位	数量	备 注


长庆工程设计有限公司

设计证书号 A161000224　　勘察证书号 B161000224

制 图			长庆油田蒙陕气田米172H区块米8井区8#煤产能建设项目地面工程
设 计			
校 对			米北-1集气站调整设计
审 核			
项目负责人			工艺自控流程图
审 定			

阶段	施工图	项目号	CEDC132S-2024
比例	~	文件号	DD24132-08-WP-PID-001-1
日期	2026-07-03	专业	给排水　版次 0版

说明：
1、本流程为米北-1集气站采出水存储及装卸车区流程图。

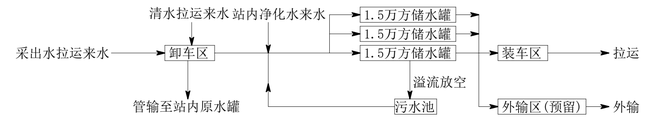

2、管线字母代号对应介质
管线、阀门编号及设备位号按照油田产建数字化交付编码规定执行。对应介质代号如下：


序号	代号	中文名称	序号	代号	中文名称
1	C	化学药剂	8	OS	含油污泥
2	RWR	循环水(回)	9	WO	污油
3	RWS	循环水(供)	10	PD	重力流排污
4	DGW	气田采出水	11	CR	地上污水罐上清液
5	TOD	处理后回注采出水	12	FRD	初期雨水
6	RW	清水	13	CRD	清洁雨水
7	RUD	回用水	14	SD	生活污水

3、字母代号功能

字母	首位功能	后继功能	字母	首位功能	后继功能
T	温 度	变 送	H	人工触发	
P	压 力		C		控 制
L	液 位		I		显 示
F	流 量		R		记 录
A	分 析	报 警	U	多变量	多功能
M	水分或湿度	中、中间	V		阀 门
S	速度或频率	开关或联锁	X	未分类	未分类
Z	状 态	驱动器、执行元件	Y		继动器、转换器

4、图形符号功能

站控系统　　现场仪表　　电信号线

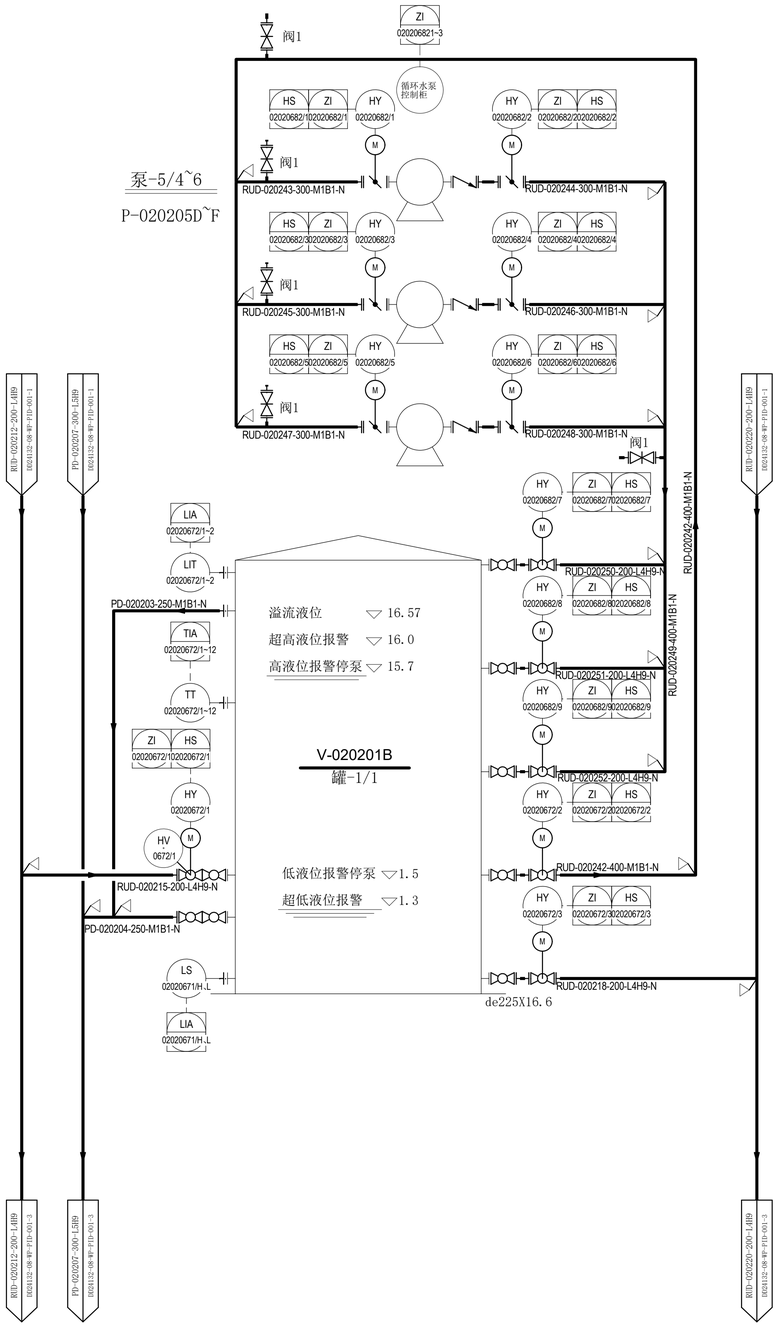

阀1	放空阀　J11H-10Q DN25	个	38	
器-1	成套加药装置(2罐2泵)	套	1	
泵-5/1~9	循环水泵 Q=400m^3/h,H=36m,N=75kW	台	9	
池-1	污水池　8mx6mx5m	座	1	
罐-1/1-3	储水罐V=15000m^3	具	3	
泵-4/1~2	污水提升泵 Q=15m^3/h,H=50m,N=5.5kW	台	2	
泵-3/1~2	装车泵　Q=120m^3/h,H=30m,N=18.5kW	台	2	
泵-2/1~2	卸水提升泵(清水) Q=120m^3/h,H=60m,N=30kW	台	2	
泵-1/1~2	卸水提升泵(采出水) Q=120m^3/h,H=60m,N=30kW	台	2	
箱-1/1-4	卸水箱 V=24m^3　6000mmx2000mmx2000mm	具	4	
编 号	名称型号及规格	单位	数量	备 注


长庆工程设计有限公司

设计证书号　A161000224　　勘察证书号　B161000224

制 图			长庆油田蒙陕气田米172H区块来8井区8＃煤产能建设项目地面工程
设 计			
校 对			米北-1集气站调整设计
审 核			
项目负责人			工艺自控流程图
审 定			


阶段	施工图	项目号	CEDC132S-2024		
比例	~	文件号	DD24132-08-WP-PID-001-2		
日期	2026-07-03	专业	给排水	版次	0版

DD24132-08-WP-PID-001-3

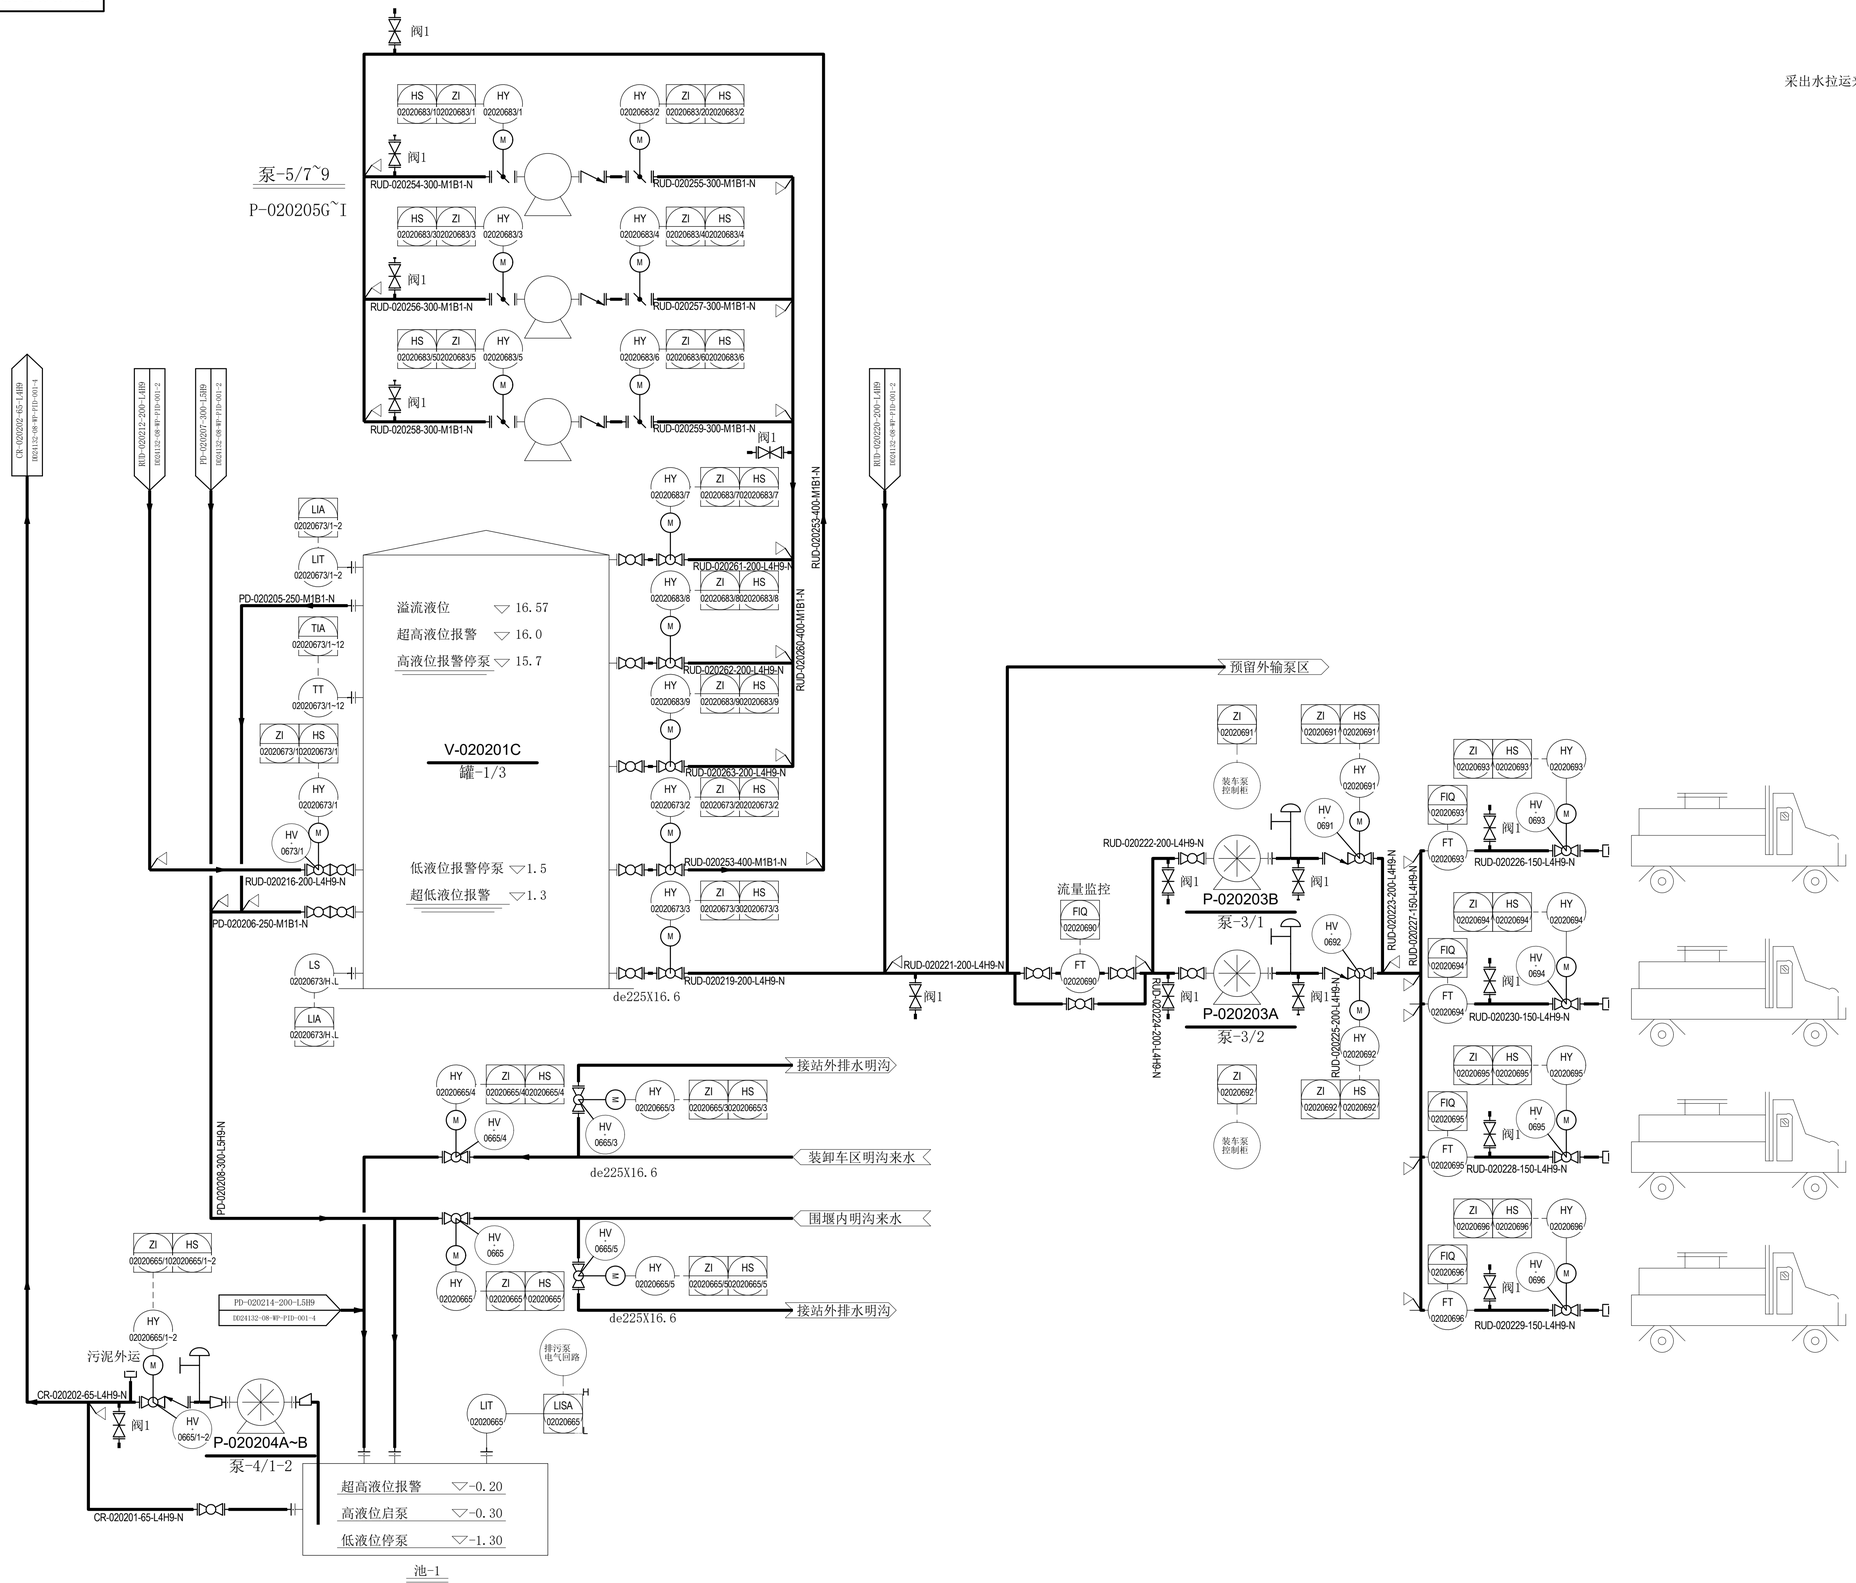

说明：

1、本流程为米北-1集气站采出水存储及装卸车区流程图。

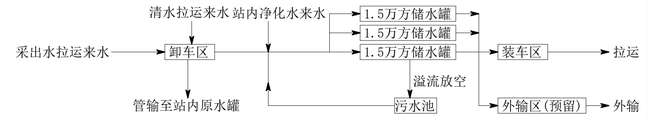

2、管线字母代号对应介质

管线、阀门编号及设备位号按照油田产建数字化交付编码规定执行。对应介质代号如下：

序号	代号	中文名称	序号	代号	中文名称
1	C	化学药剂	8	OS	含油污泥
2	RWR	循环水(回)	9	WO	污油
3	RWS	循环水(供)	10	PD	重力流排污
4	DGW	气田采出水	11	CR	地上污水罐上清液
5	TOD	处理后回注采出水	12	FRD	初期雨水
6	RW	清水	13	CRD	清洁雨水
7	RUD	回用水	14	SD	生活污水

3、字母代号功能

字母	首位功能	后继功能	字母	首位功能	后继功能
T	温 度	变 送	H	人工触发	
P	压 力		C		控 制
L	液 位		I		显 示
F	流 量		R		记 录
A	分 析	报 警	U	多变量	多功能
M	水分或湿度	中、中间	V		阀 门
S	速度或频率	开关或联锁	X	未分类	未分类
Z	状 态	驱动器、执行元件	Y		继动器、转换器

4、图形符号功能

站控系统　　现场仪表　　电信号线


阀1	放空阀　J11H-10Q DN25	个	38	
器-1	成套加药装置(2罐2泵)	套	1	
泵-5/1~9	循环水泵 Q=400m^3/h, H=36m, N=75kW	台	9	
池-1	污水池　8mx6mx5m	座	1	
罐-1/1-3	储水罐V=15000m^3	具	3	
泵-4/1~2	污水提升泵 Q=15m^3/h, H=50m, N=5.5kW	台	2	
泵-3/1~2	装车泵　Q=120m^3/h, H=30m, N=18.5kW	台	2	
泵-2/1~2	卸水提升泵(清水) Q=120m^3/h, H=60m, N=30kW	台	2	
泵-1/1~2	卸水提升泵(采出水) Q=120m^3/h, H=60m, N=30kW	台	2	
箱-1/1-4	卸水箱 V=24m^3　6000mmx2000mmx2000mm	具	4	
编 号	名称型号及规格	单位	数量	备 注

长庆工程设计有限公司

设计证书号　A161000224　　勘察证书号　B161000224


制 图			长庆油田蒙陕气田米172H区块来8井区8＃煤产能建设项目地面工程
设 计			
校 对			米北-1集气站调整设计
审 核			
项目负责人			工艺自控流程图
审 定			
			阶段　施工图　项目号　CEDC132S-2024
			比例　～　文件号　DD24132-08-WP-PID-001-3
			日期　2026-07-03　专业　给排水　版次　0版

DD24132-08-WP-PID-001-4

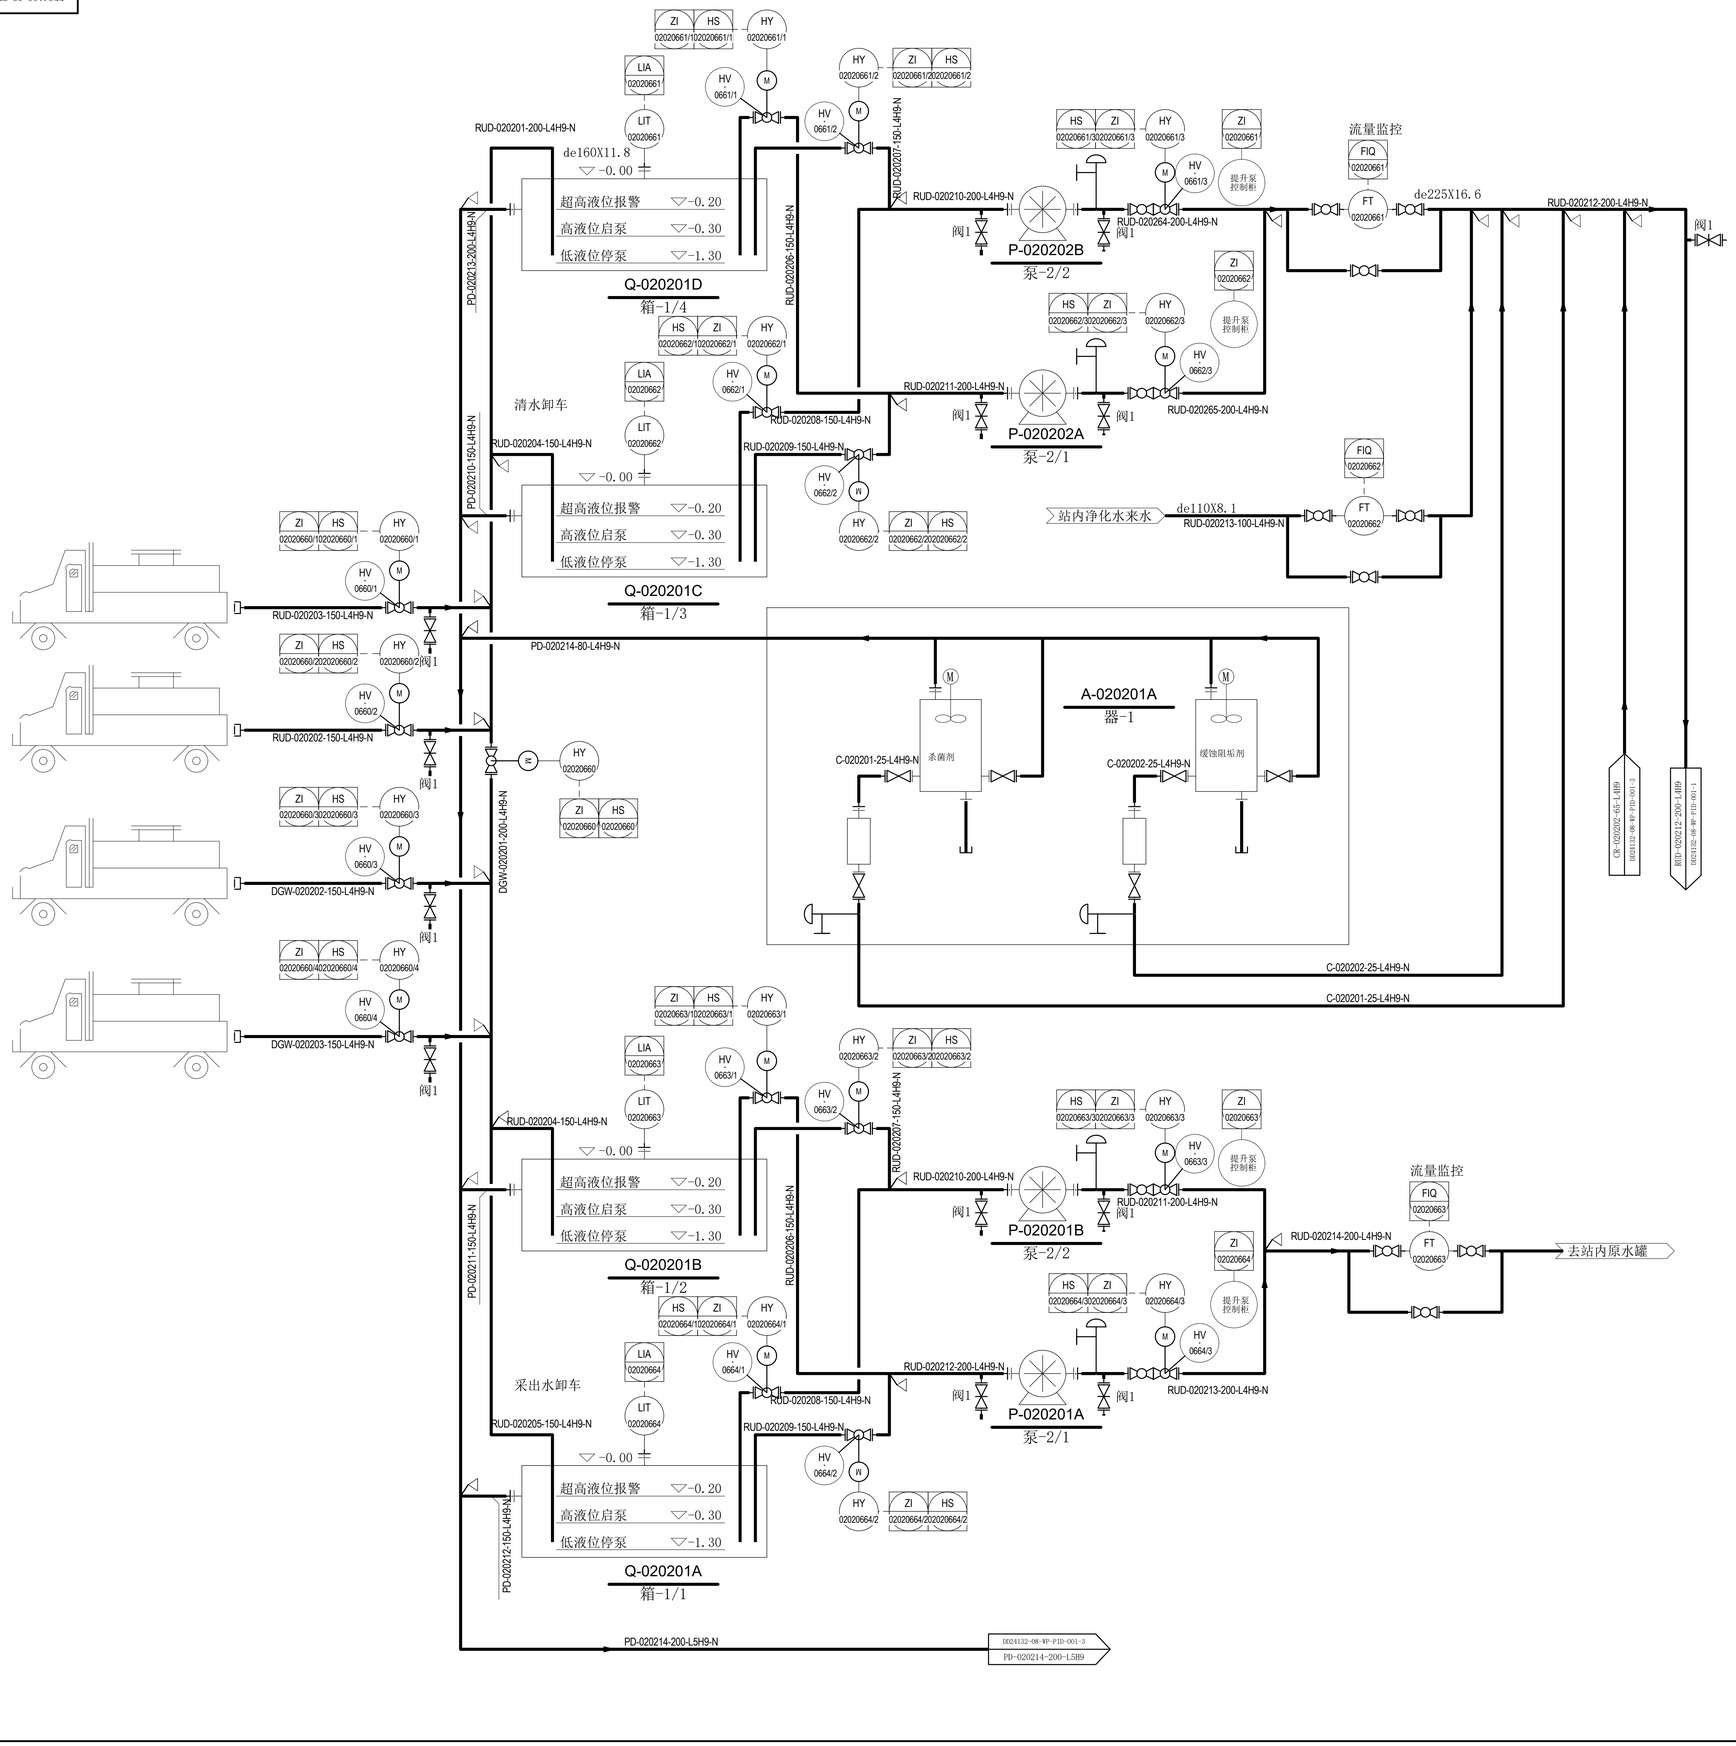

说明：

1、本流程为米北-1集气站采出水存储及装卸车区流程图。

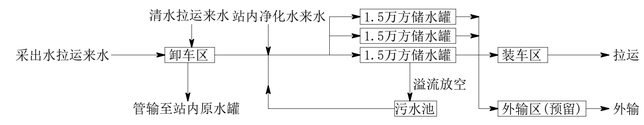

2、管线字母代号对应介质

管线、阀门编号及设备位号按照油田产建数字化交付编码规定执行。对应介质代号如下：

序号	代号	中文名称	序号	代号	中文名称
1	C	化学药剂	8	OS	含油污泥
2	RWR	循环水(回)	9	WO	污油
3	RWS	循环水(供)	10	PD	重力流排污
4	DGW	气田采出水	11	CR	地上污水罐上清液
5	TOD	处理后回注采出水	12	FRD	初期雨水
6	RW	清水	13	CRD	清洁雨水
7	RUD	回用水	14	SD	生活污水

3、字母代号功能

字母	首位功能	后继功能	字母	首位功能	后继功能
T	温 度	变 送	H	人工触发	
P	压 力		C		控 制
L	液 位		I		显 示
F	流 量		R		记 录
A	分 析	报 警	U	多变量	多功能
M	水分或湿度	中、中间	V		阀 门
S	速度或频率	开关或联锁	X	未分类	未分类
Z	状 态	驱动器、执行元件	Y		继动器、转换器

4、图形符号功能

站控系统　　现场仪表　　电信号线

阀1	放空阀　J11H-10Q DN25	个	38	
器-1	成套加药装置(2罐2泵)	套	1	
泵-5/1~9	循环水泵 Q=400m^3/h, H=36m, N=75kW	台	9	
池-1	污水池　8mx6mx5m	座	1	
罐-1/1-3	储水罐V=15000m^3	具	3	
泵-4/1~2	污水提升泵 Q=15m^3/h, H=50m, N=5.5kW	台	2	
泵-3/1~2	装车泵　Q=120m^3/h, H=30m, N=18.5kW	台	2	
泵-2/1~2	卸水提升泵(清水) Q=120m^3/h, H=60m, N=30kW	台	2	
泵-1/1~2	卸水提升泵(采出水) Q=120m^3/h, H=60m, N=30kW	台	2	
箱-1/1-4	卸水箱 V=24m^3　6000mmx2000mmx2000mm	具	4	
编 号	名称型号及规格	单位	数量	备 注

长庆工程设计有限公司

设计证书号　A161000224　　勘察证书号　B161000224

制 图			长庆油田鄂陕气田米172H区块米8井区8#煤产能建设项目地面工程
设 计			
校 对			米北-1集气站调整设计
审 核			
项目负责人			工艺自控流程图
审 定			

阶段	施工图	项目号	CEDC132S-2024
比例	~	文件号	DD24132-08-WP-PID-001-4
日期	2026-07-03	专业	给排水　版次　0版