
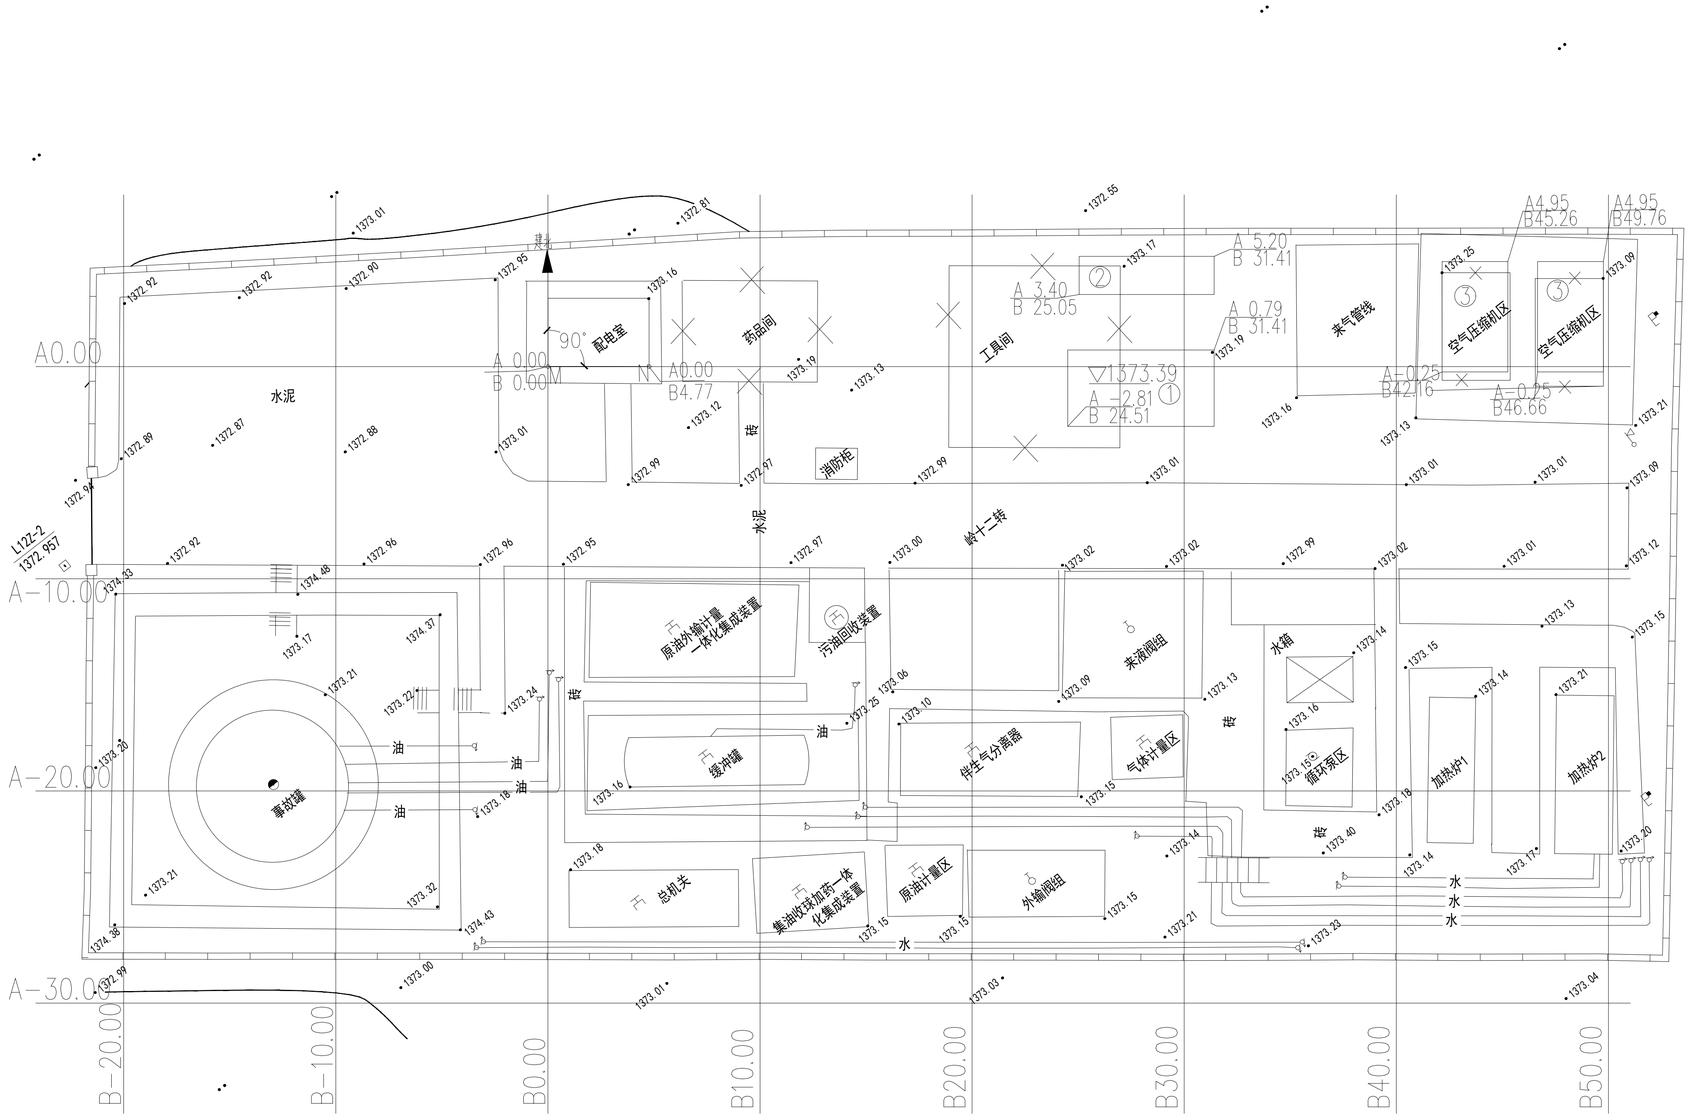


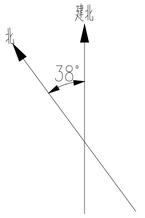

说 明:

1、高程系统采用1985国家高程基准。建北方向与北方向夹角为12°。

2、图中坐标、标高以米计。

3、本次设计以已建药品间西南角为(A 0.00,B 0.00)、以M(A0.00,B0.00)和N(A 0.00,B 4.77)两点为准进行放线,两点连线长度为4.77m,与建北方向夹角为90°。

4、× 表示拆除,拆除站内原已建药品间、工具间等,具体详见拆除设施一览表。

5、 输油泵基础高出所在地坪100mm,伴生气压缩机高出所在地坪200mm。

拆除工程量

序号	名称及规格	单位	数量	备注
1	药品间	处	2	
2	工具间	具	1	
3	伴生气压缩机(含基础)	座	1	

编号	名称型号及规格	单位	数量	单体文件号	备注
③	伴生气压缩机	台	2		外购防爆型 站内迁建
②	流量计(来油)-2.5-100/80	座	1		
①	离心泵 Q=70m/h H=400m	台	1		配防爆电机 N=160kW/台

建(构)筑物一览表

长庆工程设计有限公司

设计证书号 A261000221 勘察证书号 B161000224

制 图		长庆油田页岩油2026年产建地面工程
设 计		里180区长7页岩油2025年产能建设项目地面工程 骨架工程站场(一) 平面布置图
校 对		
审 核		
项目负责人		
审 定		

阶段	施工图	项目号	CEDC151C-2025		
比例	1:200	文件号	BD25151-0102-OP-PLA-001		
日期	2025.7.7	专业	油气集输	版次	A 版